



L/S BEAM B111 (230x425)

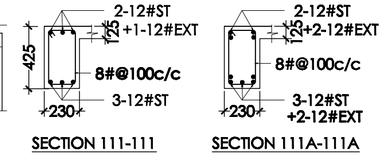


SECTION 111-111


SECTION 111A-111A

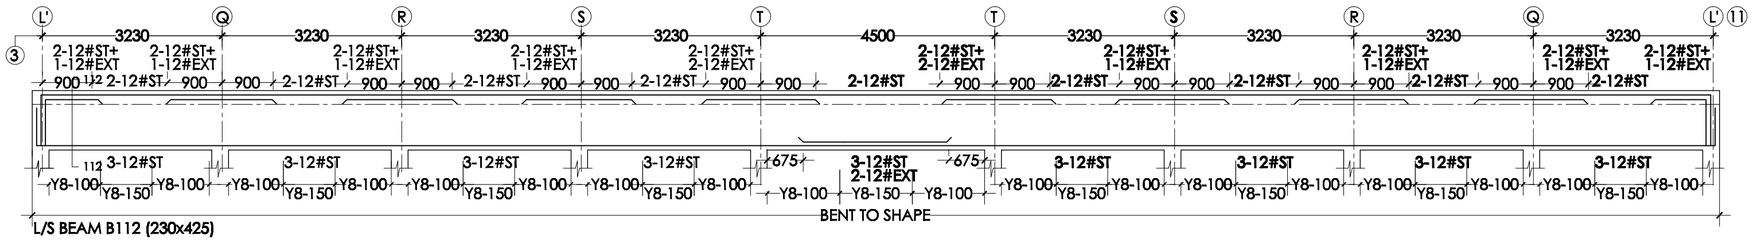


L/S BEAM B112 (230x425)

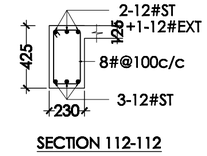


SECTION 112-112

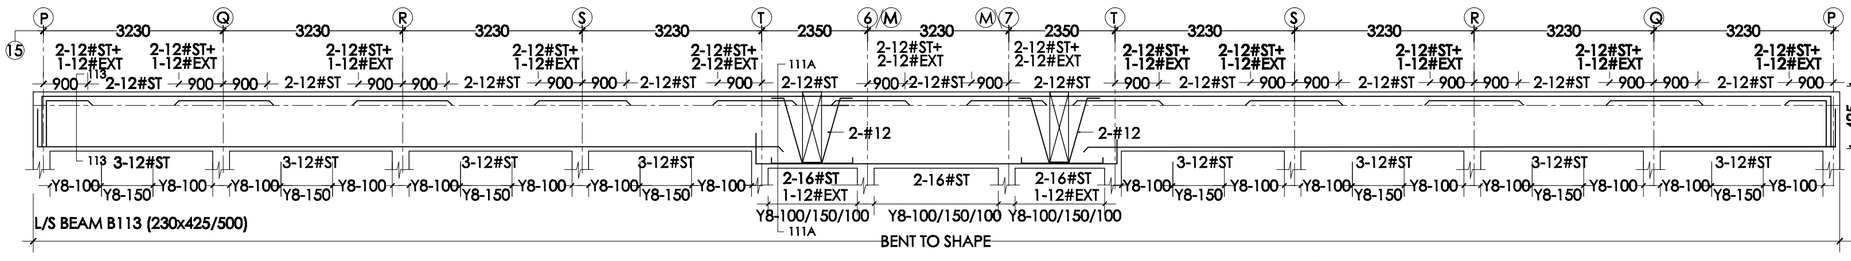


L/S BEAM B113 (230x425/500)

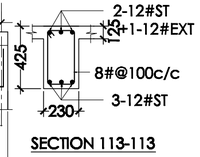


SECTION 113-113

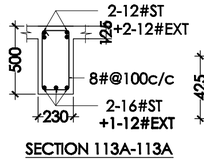


SECTION 113A-113A

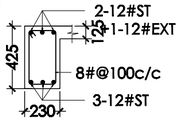


SECTION 114-114

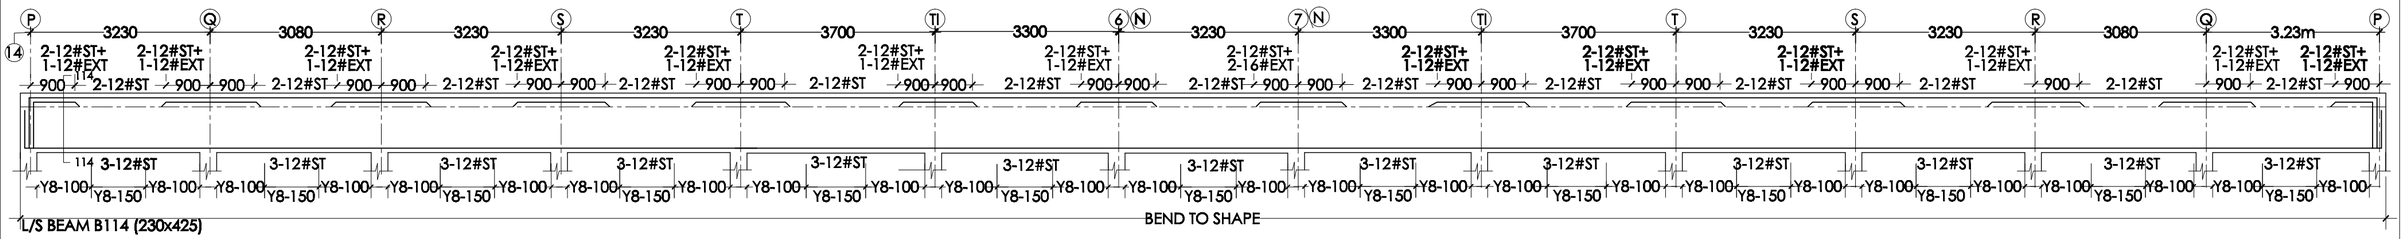


L/S BEAM B114 (230x425)

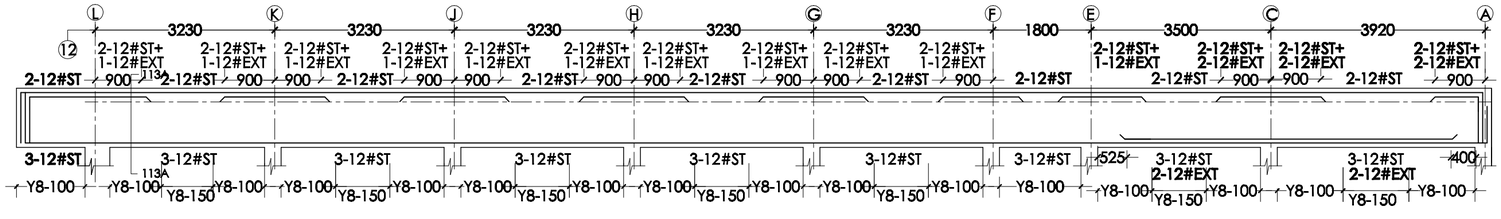


L/S BEAM B113A (230x425)

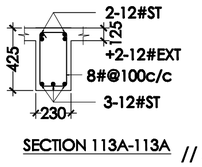

SECTION 113A-113A

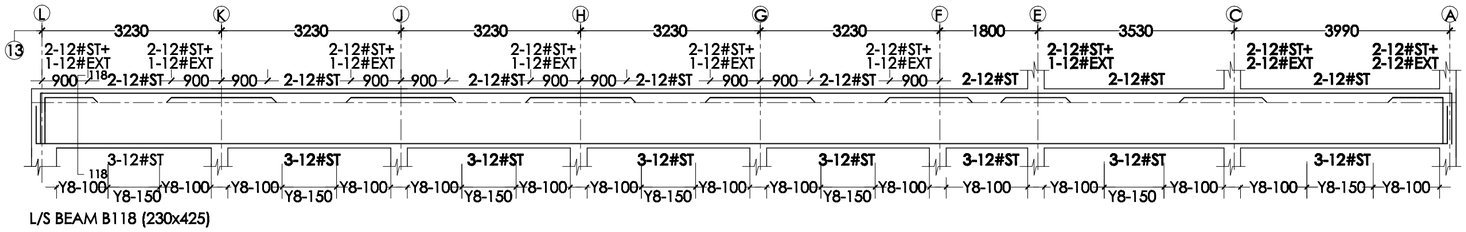

L/S BEAM B118 (230x425)

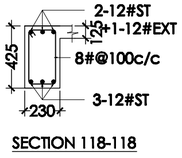

SECTION 118-118

// APPROVED //
SD/- Sri K. Venkateshwara rao
Chief Engineer
DT: 25-09-2011
SPO / RVM / HYD

// TCF BO //

State Project Engineer
SPO / RVM / HYD

CLIENT: RAJIV VIDYA MISSION

PROJECT:

CONSTRUCTION OF KGBV SCHOOL BUILDING EXCLUSIVELY FOR GIRLS STUDENTS FOR VI TO X CLASSES -

TITLE:

FIRST FLOOR ROOF BEAM L/S DETAILS STRUCTURAL

DATE: 25-09-2011 | ALTERNATIVE 01

DRG. No: 120 (sheet 2 of 4)

ARCHITECTURAL CONSULTANTS:

SITE 2 HEIGHT
Architects, Engineers, Interiors, 2D Digitization
Regn no: CA/2003/31400 A.I.I.A, C.A
Room:316 Omar Building, H-no:3-3-39 Kachiguda Station Road, Hyderabad -27 A.P
mobile: 9246375890 phone: 040-55305890 E-mail: ar_subhani@yahoo.com

Drg. No. 120 / RVM / CWS / KGBV / S2H - Alt - I / 2011-12, Sheet 2 of 4, Rev.01, Dated 25-09-2011